


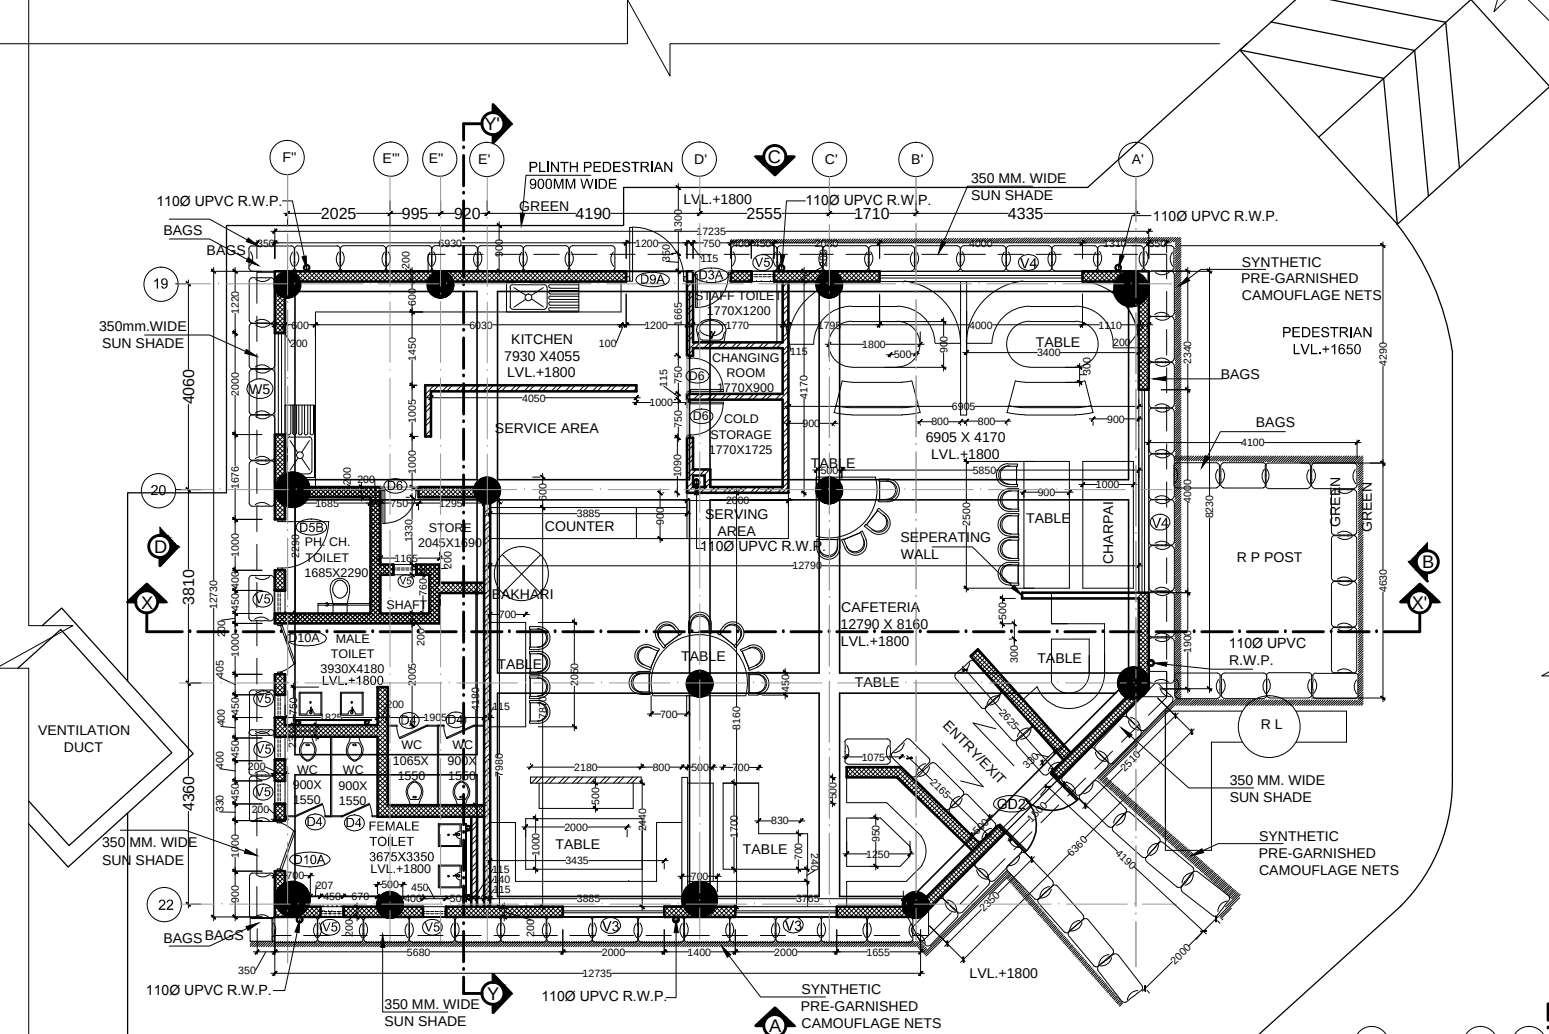


CAFETERIA (GROUND FLOOR PLAN)

GREEN

PEDESTRIAN LVL.+1650

LVL.+1800

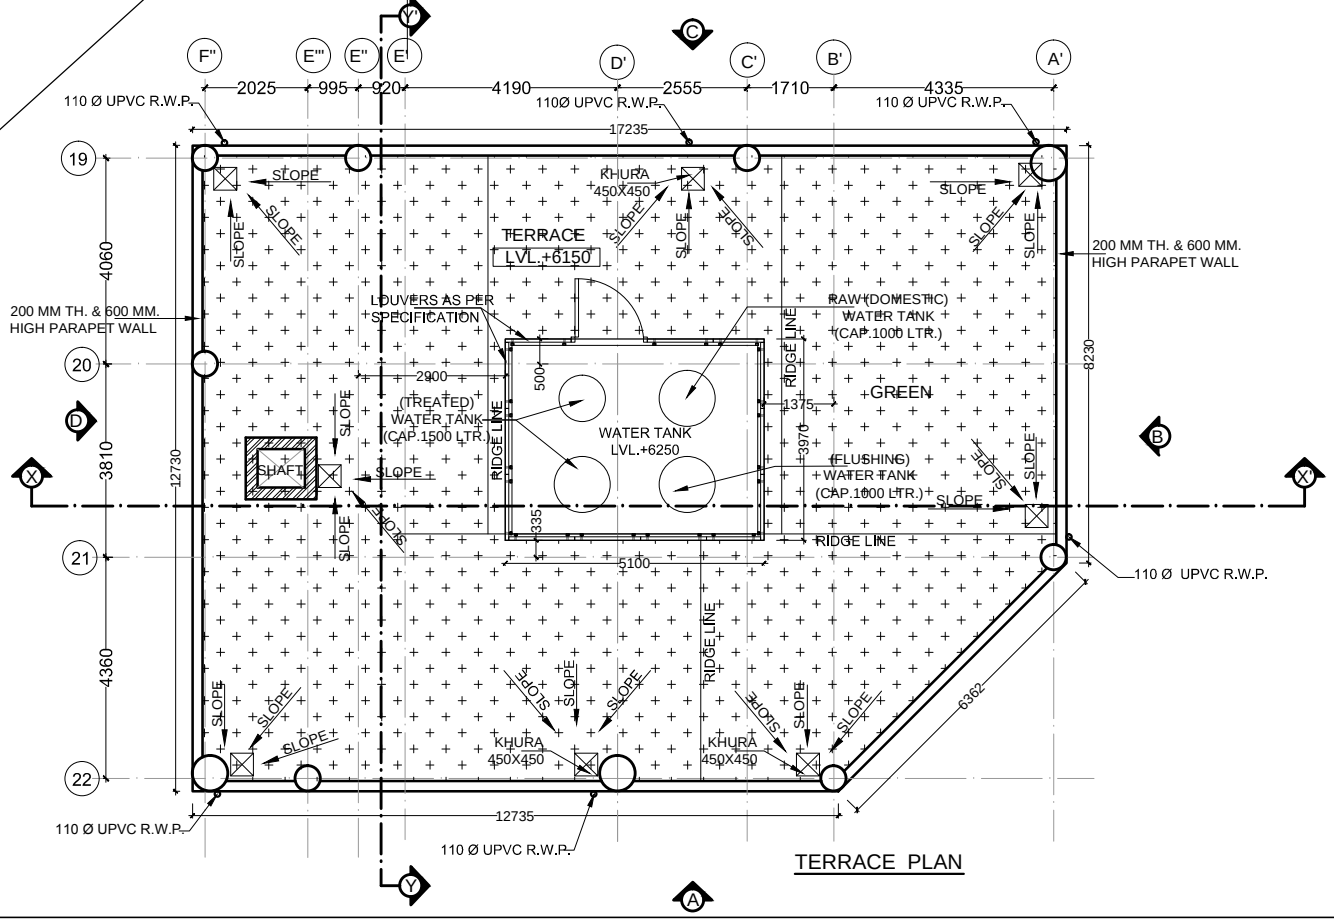

TERRACE PLAN

DOORS & WINDOWS SCHEDULE OF OPENING'S


S.NO.	TYPE	SIZE	SILL LEVEL	LIN. LEVEL	REMARKS.
1	GD2	2000X2400	00	2400	12MM CLEAR FRAMELESS TOUGHENED GLASS DOOR (DOUBLE LEAF)
2	D3A	750X2400	00	2400	LAMINATED WOODEN FLUSH DOOR (SINGLE LEAF)
3	D4	600X1830	205	-	COMPACT LAMINATED SINGLE SHUTTER DOOR
4	D5B	1000X2400	00	2400	LAMINATED WOODEN FLUSH SWING DOOR (SINGLE LEAF)
5	D6	750X2400	00	2400	ALUMINIUM DOOR WITH PRE-LAMINATED BOARD (SINGLE LEAF)
6	D9A	1200X2400	00	2400	LAMINATED WOODEN FLUSH DOOR WITH VISION PANEL (SINGLE LEAF)
7	D10A	1000X2400	00	2400	LAMINATED WOODEN FLUSH DOOR (SINGLE LEAF)
8	W5	2000 X 1200	1200	2400	ALUMINIUM FRAME GLAZED SLIDING WINDOW
9	V3	2000 X 600	900	1500	ALUMINIUM FRAME FIXED GLAZING
10	V4	4000 X 600	900	1500	ALUMINIUM FRAME FIXED GLAZING
11	V5	450 X 450	1950	2400	ALUMINIUM FRAME GLAZED VENTILATOR

LEGEND :-

1		C.C. BLOCKS
2		BRICK WORK

NOTE:-
(1) DISCREPANCY IF ANY ,SHOULD BE BROUGHT TO THE NOTICE OF ARCHITECT.
(2) ALL DIMENSIONS ARE IN MM.
(3) DRAWINGS ARE BEING ISSUED ASSUMING THAT DRAWINGS ARE APPROVED BY P.W.D. AND NO APPROVAL OF LOCAL BODY IS REQUIRED.
(4) SYNTHETIC PRE-GARNISHED CAMOUFLAGE NETS USED IN THE EXTERIORS TO BE EXECUTED AS PER DIRECTIONS FROM ARCHITECT ON SITE.

KEY PLAN-

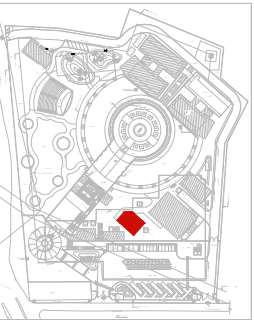

R4	05-08-2015	REVISED AS PER VARIOUS MEETING HELD AT SITE WITH SANKU WELFARE OFFICIALS AND COL. RAVINDER NEERA.
R3	31-07-2014	DRAWING REVISED AS DIRECTED BY CHIEF ARCHITECT PWD.
R3	31-07-2014	DRAWING REVISED AS DIRECTED BY CHIEF ARCHITECT PWD.
R2	09-07-2014	MOVED TO AS PER THE COMMENTS IN PROOF CHECKED.
R1	25-06-2014	DRAWING REVISED FROM THAPAR UNIVERSITY.
S. NO.	DATE	REMARKS
GOOD FOR CONSTRUCTION ☒ FOR SUBMISSION PURPOSE ☐		
OWNER'S		ARCHITECT
PROJECT :- DEVELOPMENT OF PROPOSED WAR MEMORIALCUM MUSEUM NEAR SHAM SINGH ATTARI WALA CHOWK ON AMRITSAR - ATTARI ROAD		
CLIENT :- DIRECTOR DEFENCE SERVICES WELFARE OF PUNJAB, PUNJAB SAINIK BHAWAN, SECTOR-21D, CHANDIGARH		
CONSULTANT :- KAPOOR & ASSOCIATES ARCHITECTS, ENGINEERS & PLANNERS AD-110-C, RING ROAD, SHALIMAR BAGH, DELHI. 110088 INDIA. PH: 011-27480514,27487604 E-Mail: associateskapoor@gmail.com Website: www.kapoorandassociates.com		
TITLE :- GROUND & TERRACE FLOOR PLAN (CAFETERIA)		
SCALE :- 1:100		
DATE :- APR. 2016		
DRG. NO:- KAWM/CF-01(R4)		
DRAWN BY :- Sojo		
CHK BY :- V.P.		
THIS DRAWING AND DESIGN IS THE PROPERTY OF KAPOOR & ASSOCIATES, AND WILL NOT BE REPRODUCED, COPIED, LOANED, EXHIBITED, USED EXCEPT WITH THE WRITTEN CONSENT OF KAPOOR & ASSOCIATES		